


DRAWING NOT TO BE SCALED FOR ACCURATE SETTING OUT.
ALL DIMENSIONS TO BE CHECKED ON SITE. PROPOSALS SUBJECT TO LOCAL AUTHORITY APPROVALS.
THIS DRAWING IS TO OBTAIN PLANNING AND OR BUILDING REGULATIONS ONLY.
ALL WORKS ON OR WITHIN A 3 MTR ZONE OF A NEIGHBOURING BOUNDARY ARE TO BE NOTIFIED 14
DAYS BEFORE COMMENCEMENT ON SITE IN ACCORDANCE WITH THE PARTY WALL ACT 1996

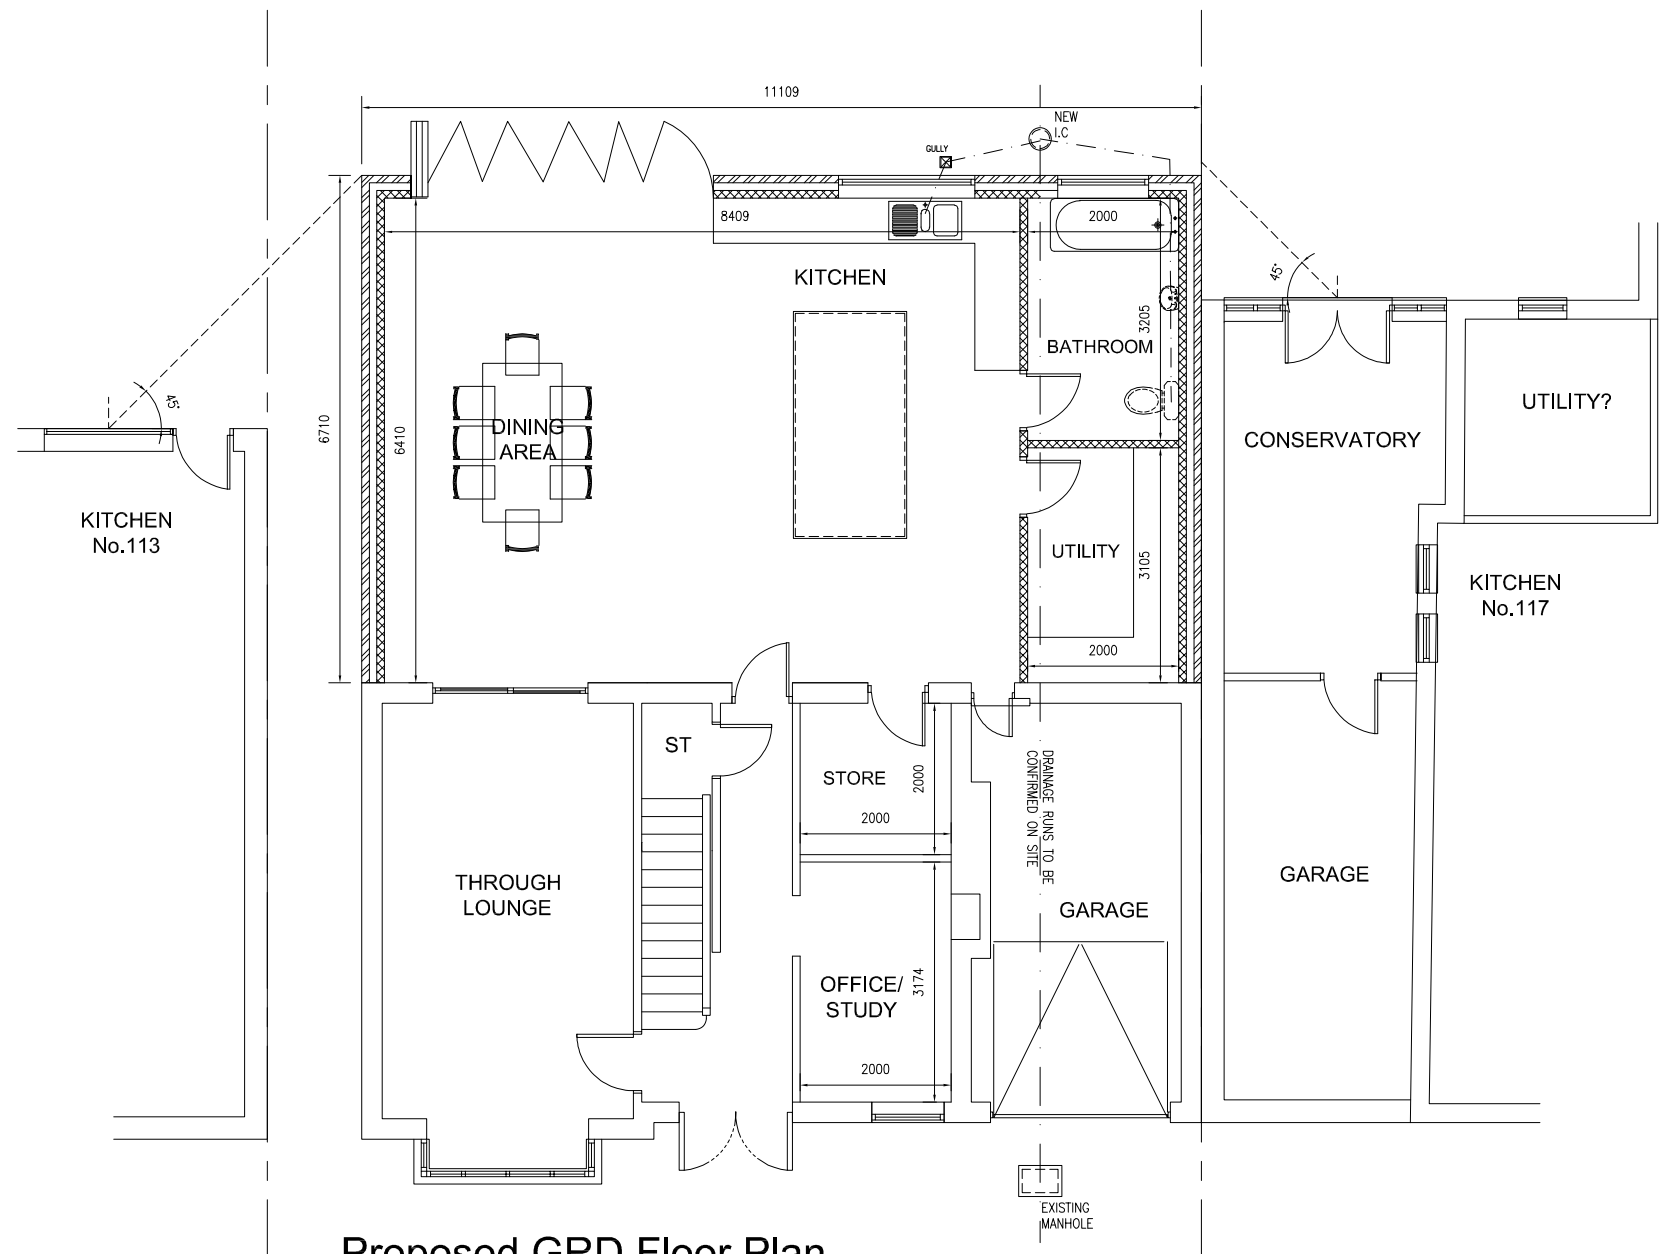

Proposed GRD Floor Plan

COLUMN/BEAM SCHEDULE


REF	LINTEL CODE	LENGTH	NUMBER OFF
B1	T.B.C	SITE MEASURE	1
B2	T.B.C	SITE MEASURE	1
L1	STRESSLINE CONCRETE LINTEL OR SIMILAR APPROVED	SITE MEASURE	IF REQUIRED

NOTE:
CAVITY WALLS TO HAVE STEEL IG LINTELS OR SIMILAR APPROVED.
SOLID BRICKWORK WALLS TO HAVE IG BOX LINTELS OR SIMILAR APPROVED U.N.O.


NOTE:
EXACT DIMENSIONS FOR LENGTH
TO BE CONFIRMED ON SITE
PRIOR TO MANUFACTURE.

NOTE
New masonry wall leafs tied to
existing using Halfen wall
starters or similar fixed to
manufacturer details.

NEW FOUNDATIONS
Trenches for new foundations
near existing party walls to be
excavated in max.1m wide bays
and hit and miss alternative bays,
so as not to compromise existing
structures.

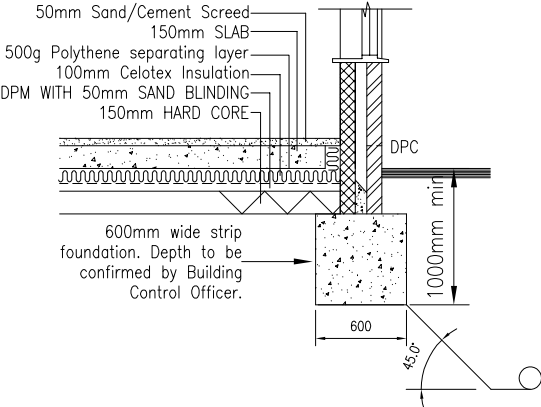

TYPICAL SECTION
Scale 1:50

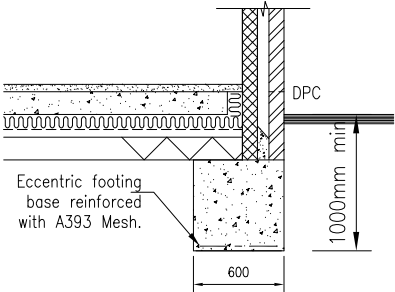

BOUNDARY SECTION
Scale 1:50

-	-	-	RA	-
Rev:	Description:	Date:	By:	Chkd:
DPC Ltd Design Plan & Construction Ltd Architectural & Structural Engineering Services Tel: 07815575110 email: DPC-Ltd@outlook.com				
APPROVAL				
Project: 115 Vicarage Rd, Birmingham, B14 7QG				
Drg Title: PROPOSED PLANS				
Scale: 1:100	Size: A3	First Issue: 19.08.26	Drawn: RA	Checked: -
Drg No: S01				Rev: -